
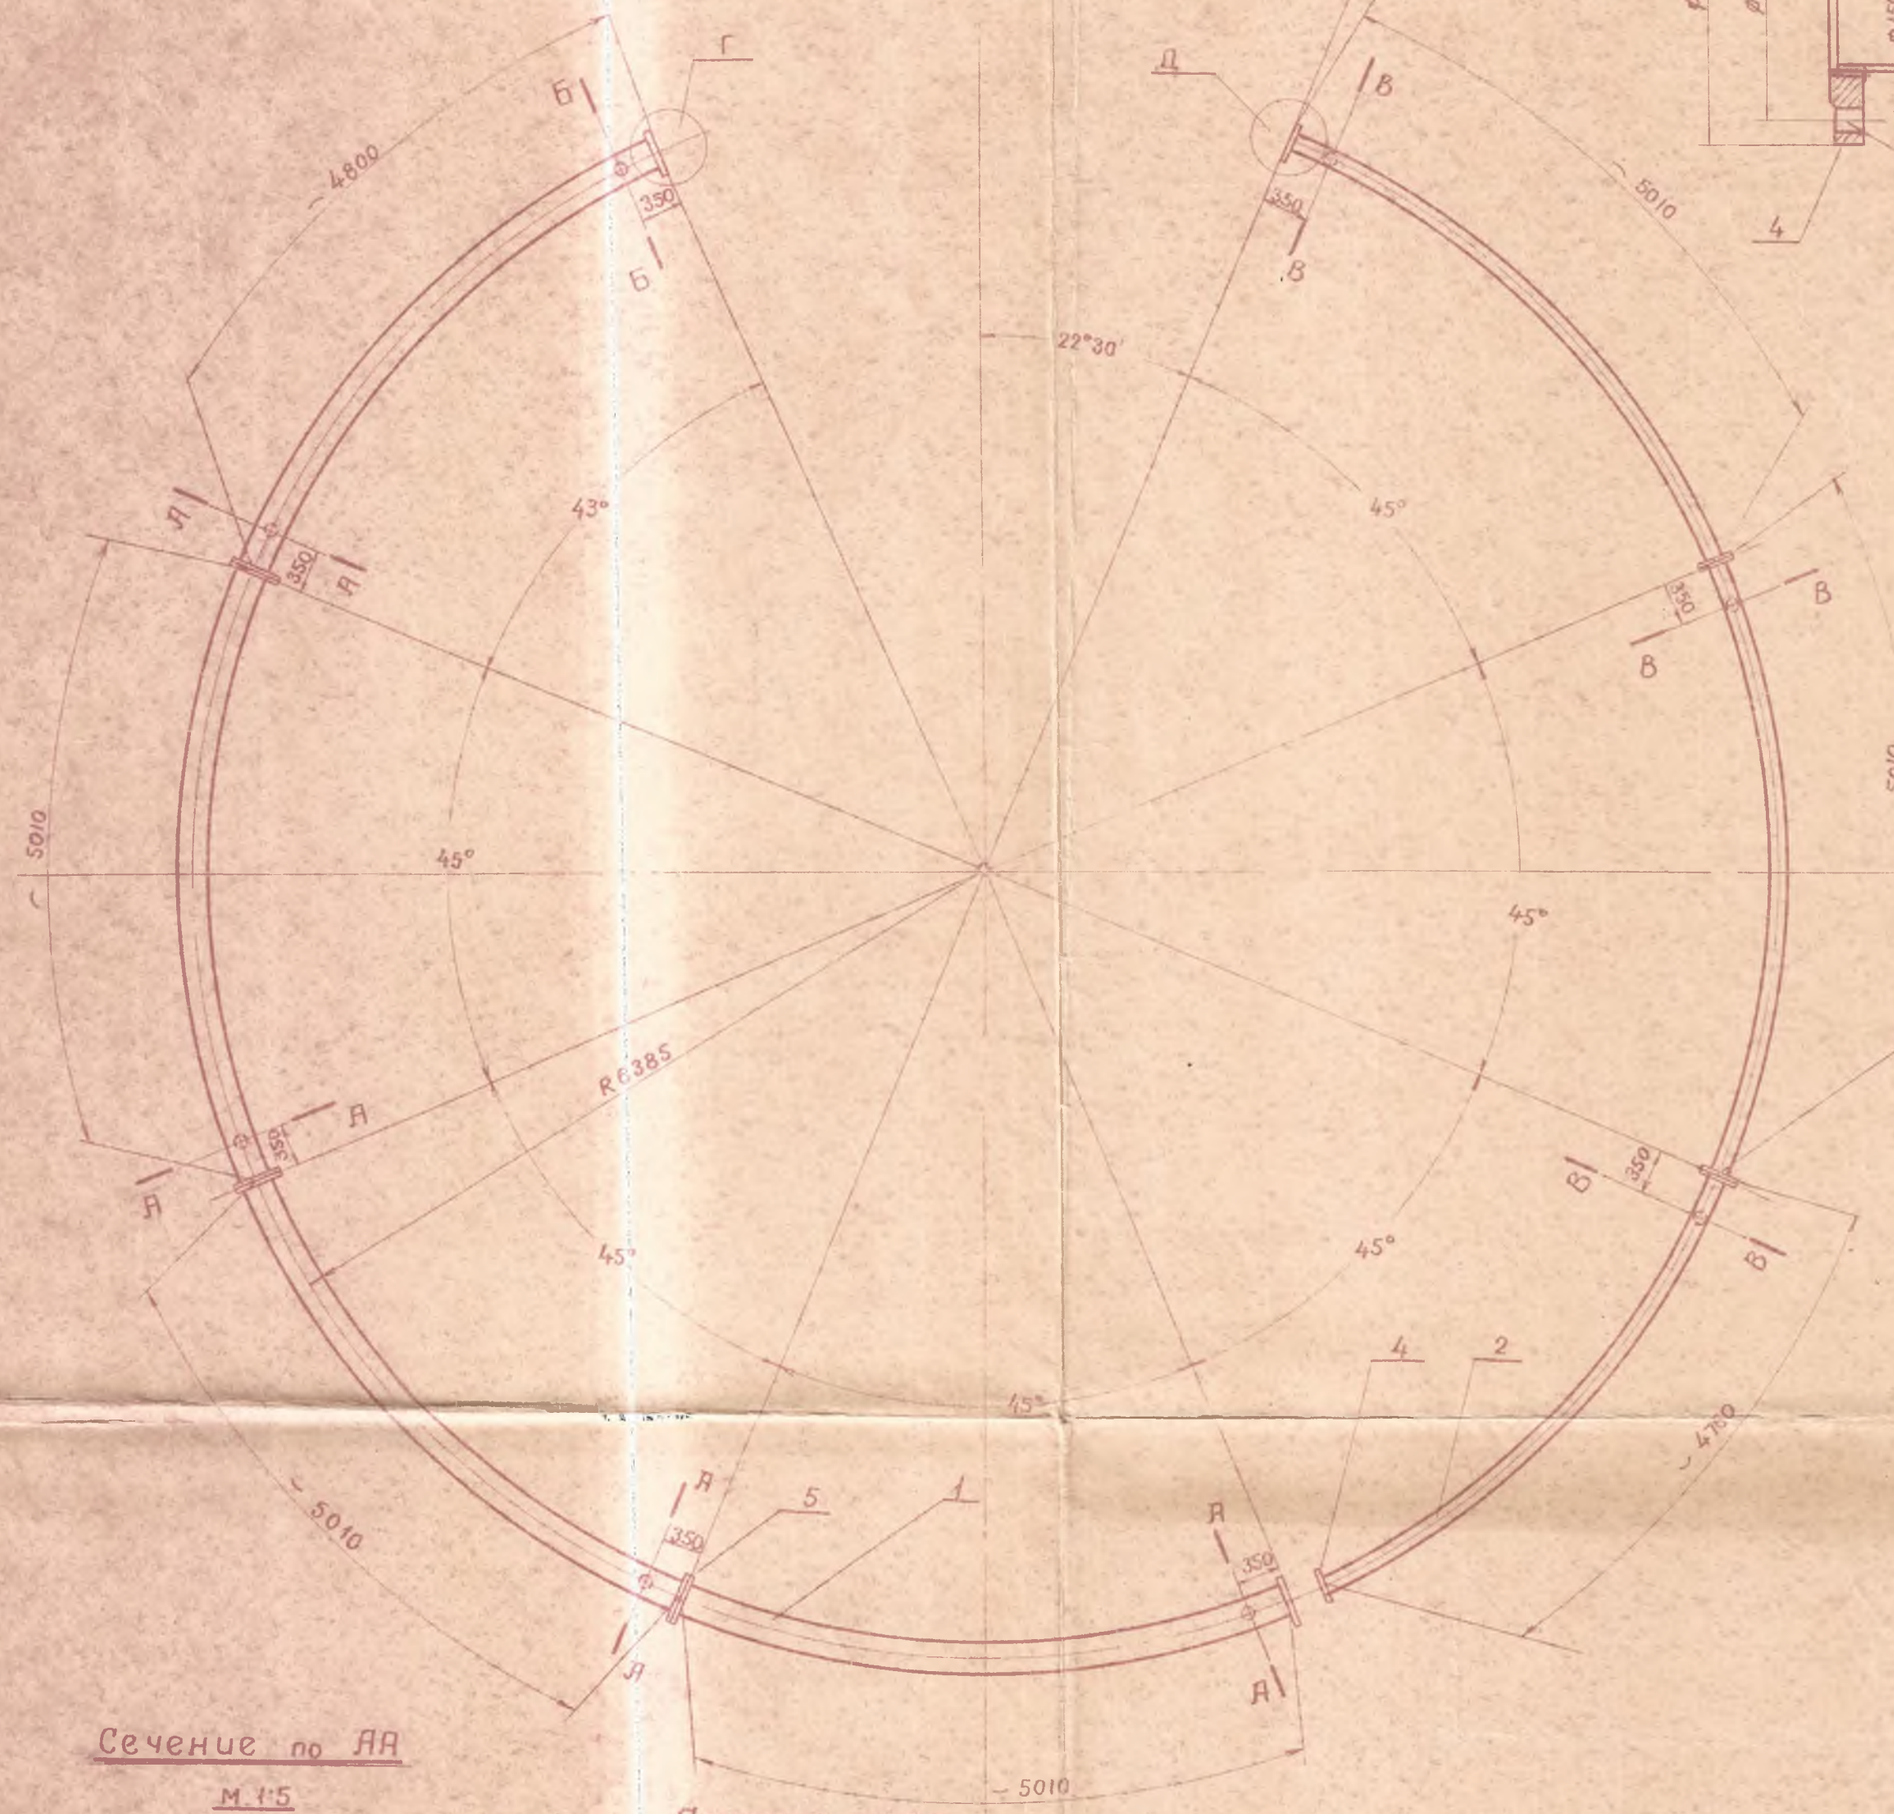



Узел Д

М 1:5

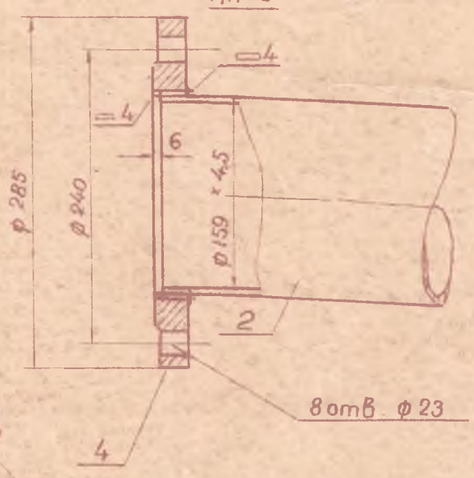


Сечение по АА

М 1:5

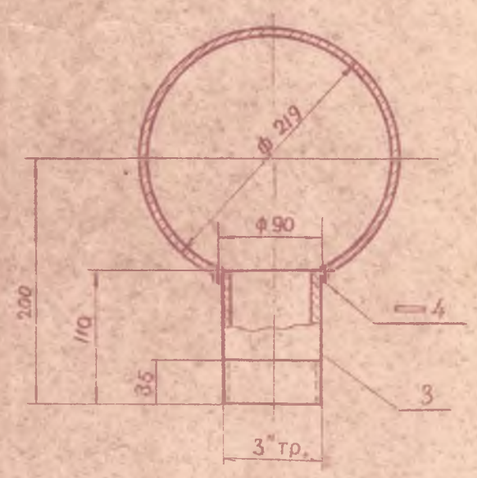


Сечение по ББ

М 1:5

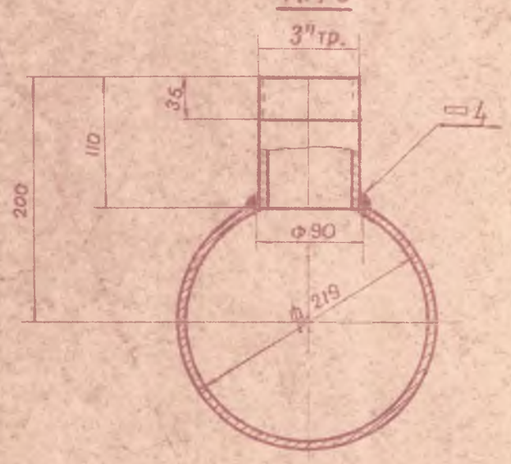


Сечение по ВВ

М 1:5

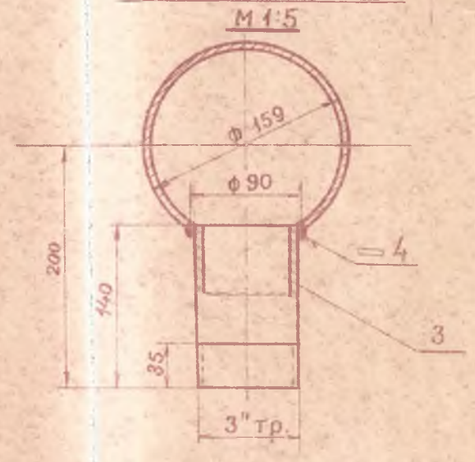

Узел Г

М 1:5

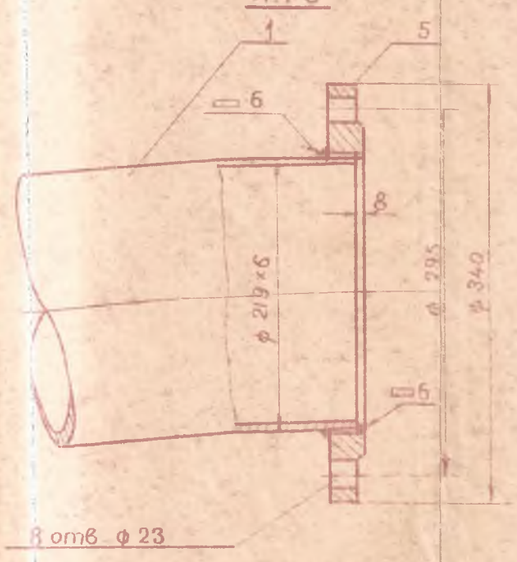

Примечание:

спесификация составлена на один коллектор.

№ поз	Наименование	Мат.	Кол.	Вес в кг: 1 шт	Вес в кг: Общ.	ГОСТ Черт. или ОСТ	Примеч.
	Наплавленный металл	Э-34			5,00	ГОСТ 2523-51	
5	Фланец стальной приварной ф 340/221×26	ст	8	10,1	80,8	ГОСТ 1257-41	
4	Фланец стальной приварной ф 285/161×26	ст	6	8,3	49,8	ГОСТ 1257-41	
3	Труба стальная газовая 3" п.м.	ст	1.0	8,34	8,34	ГОСТ 3262-46	
2	Труба стальная бесшовная ф 159×4,5 п.м.	ст	15	17,15	257,25	ГОСТ 301-50	
1	Труба стальная бесшовная ф 219×6 п.м.	ст	20	31,52	630,4	ГОСТ 301-50	
					Теорет	1031,59	
					Действ.		

Масшт.	Констр.	штяйма		Нач. Сект.	Л.О. Гидроэнергопроект Сектор турбин и металлических конструкций
1:50	Провер.				
1:5	Рук. груп.				
	Гл. спец.				

Напорный коллектор системы охлаждения генератора

К черт. № 530-3-33

№ 530-3-81

11-1/44