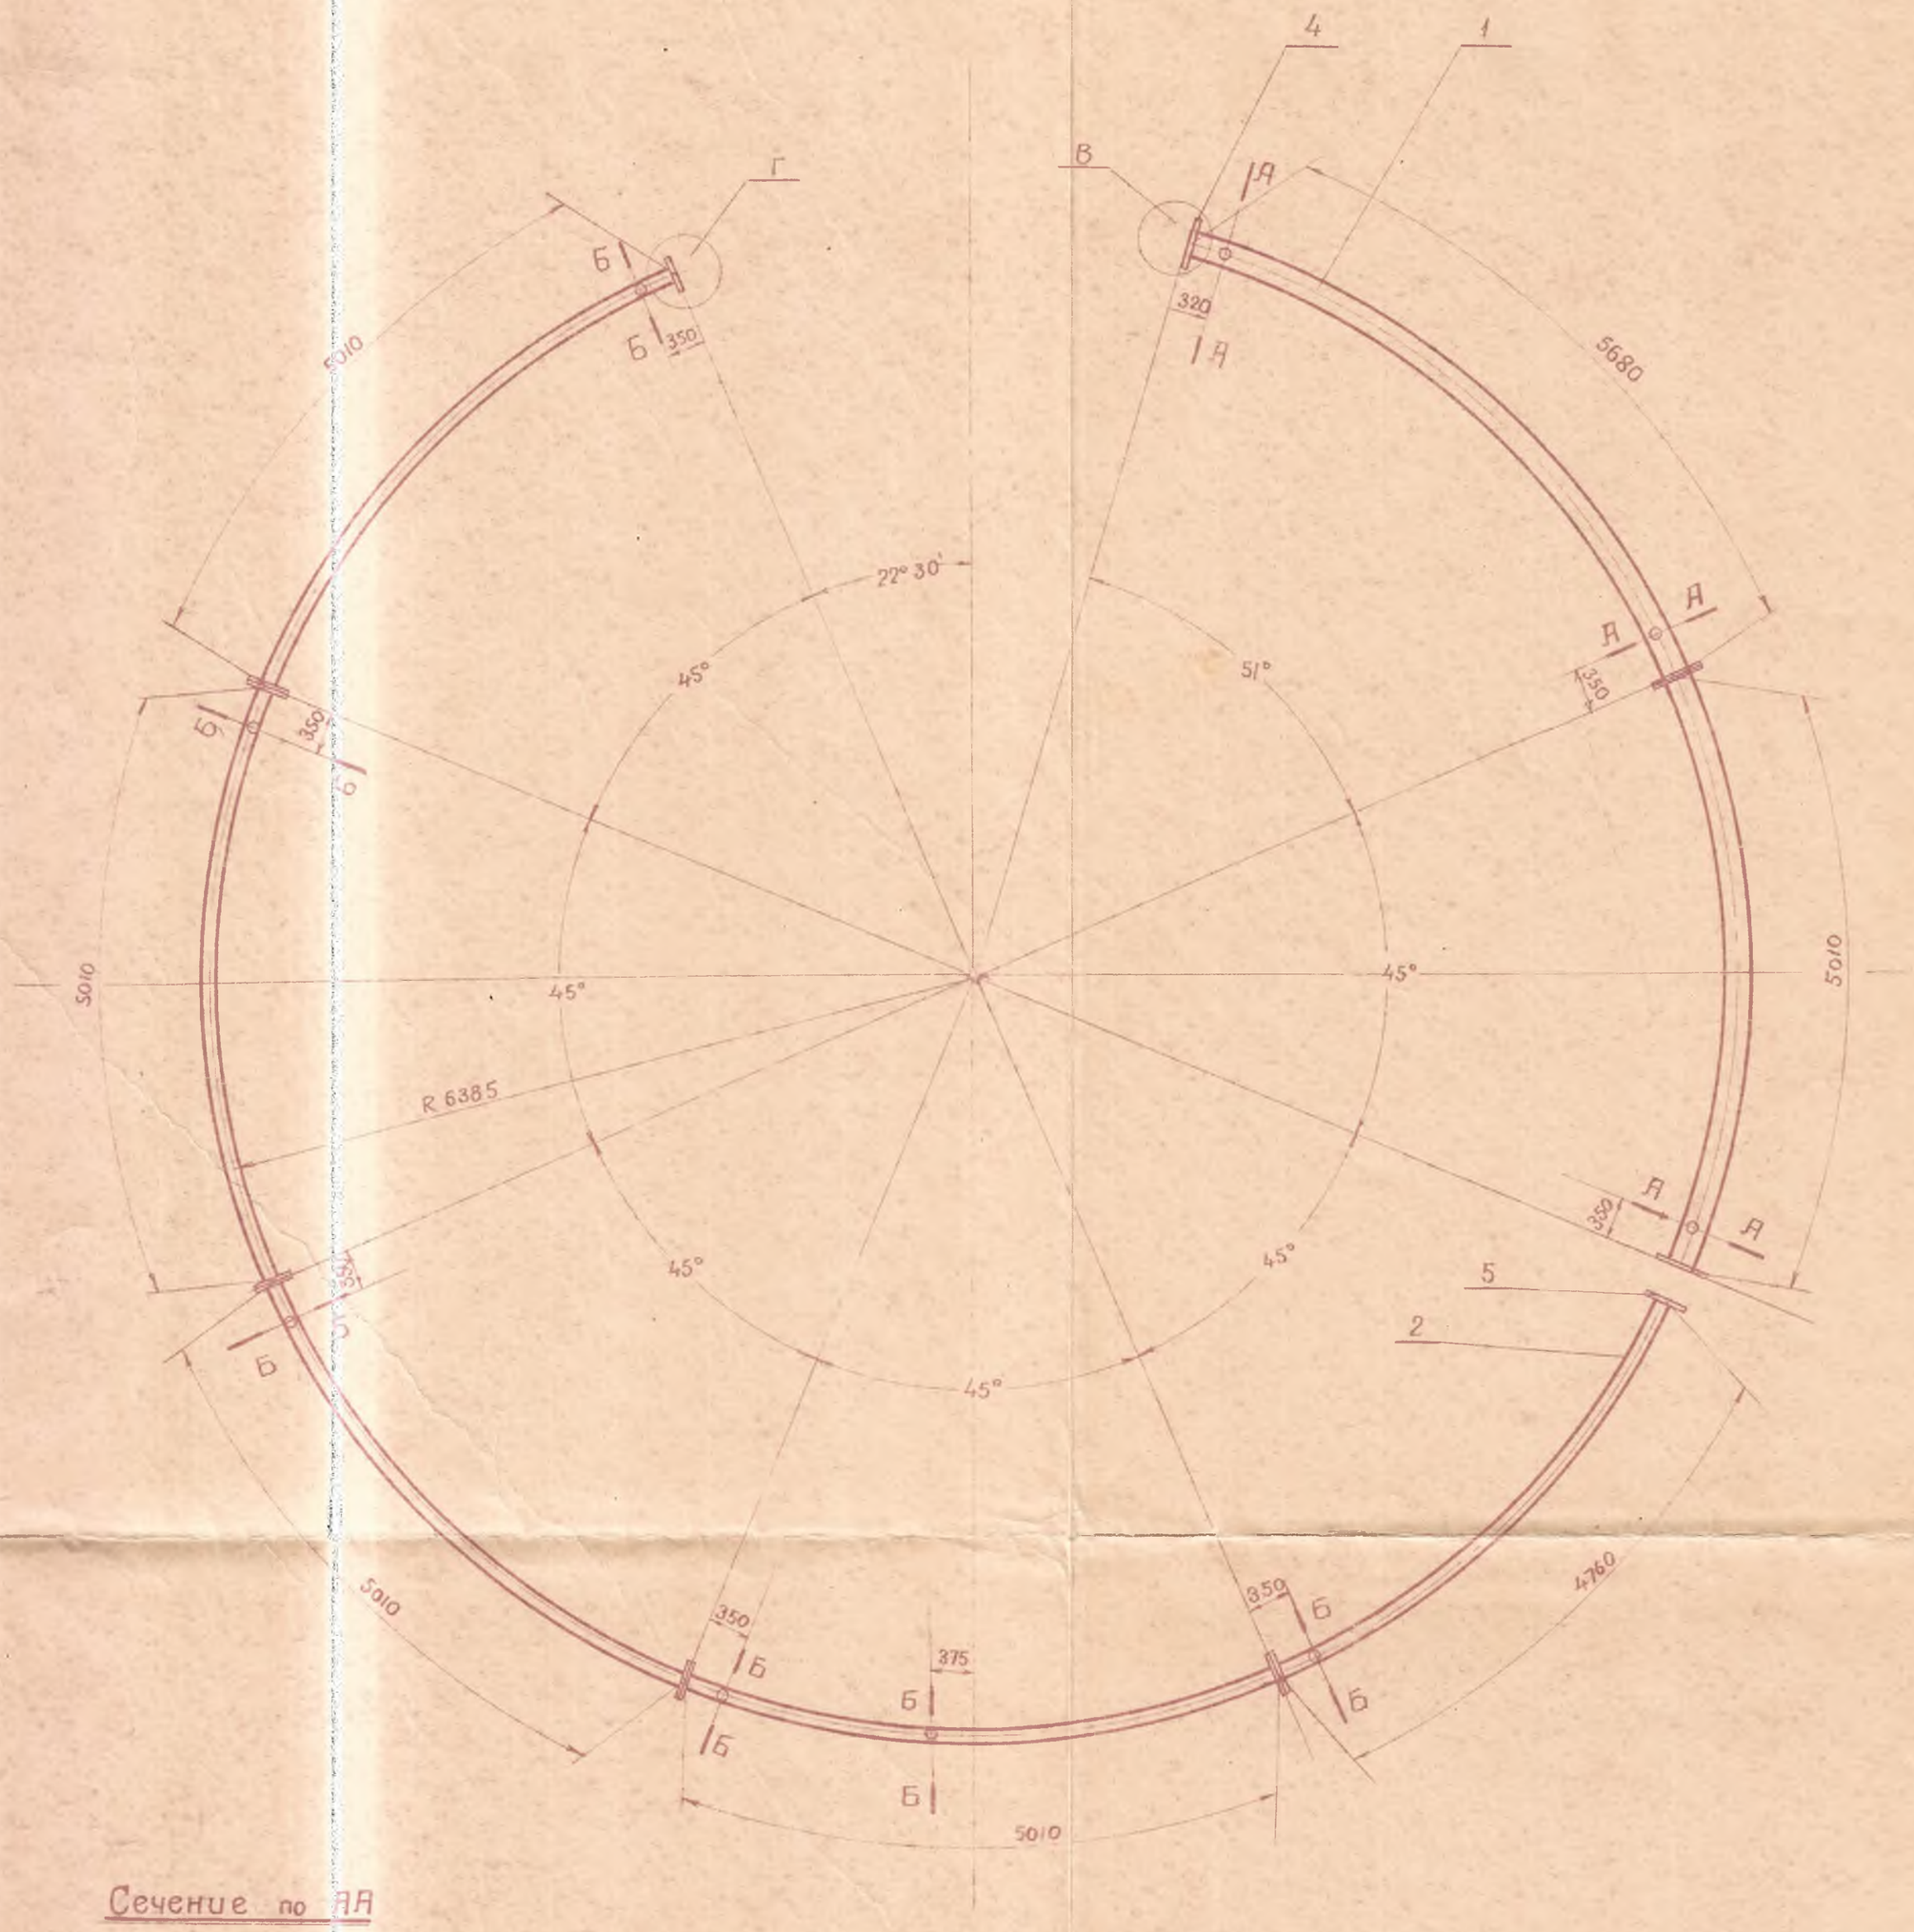



М-1/45


Сечение по АА

М.1:5

Узел В


М.1:5

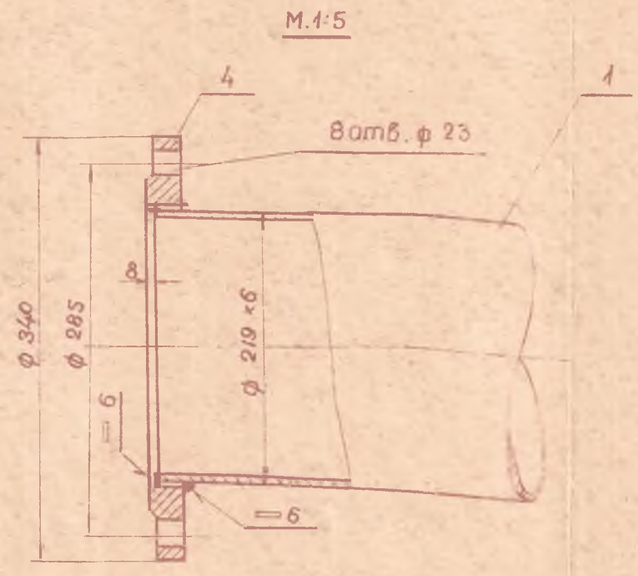

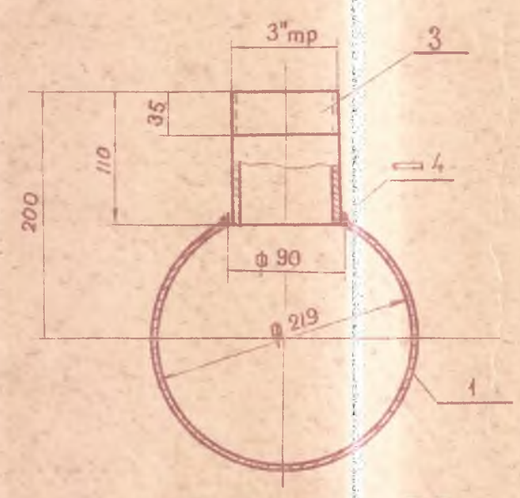


Сечение по ББ

М1:5

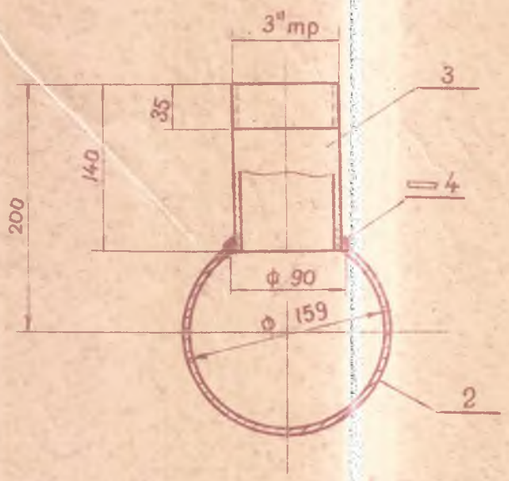

Узел Г

М.1:5

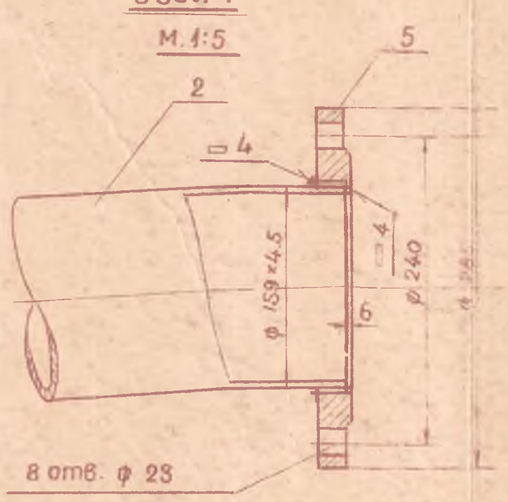

Примечание:

спесификация составлена на один коллектор.

NN поз	Наименование	Мат.	Кол.	1 шт.	Общ. вес в кг	Черт. или ост	Примеч.
	Наплавленный металл	Э-34			4,5	ГОСТ 2523-51	
5	Фланец стальной приварной ф 285/161×26	ст.	10	8,3	83,0	ГОСТ 1257-41	
4	Фланец стальной приварной ф 340/221×26	ст.	4	10,1	40,4	ГОСТ 1257-41	
3	Труба стальная газовая 3"	ст.	1.5	8,34	12,5	ГОСТ 3262-46	
2	Труба стальная бесшовная ф 159×4.5	ст.	25	17,15	428,7	ГОСТ 301-50	
1	Труба стальная бесшовная ф 219×6 п.м.	ст.	11	31,52	346,7	ГОСТ 301-50	
					Теорет.	915,80	
					Действ.		

Масшт.	Констр.	Шляхина		Нач. Сект.	Л.О. Гидроэнергопроект Сектор Турбин и металлических конструкций
1:50	Провер.				
1:5	Рук. Груп.				
	Гл. спец.				

Сливной коллектор системы охлаждения генератора

К черт. N 530-3-33

N 530-3-82